


SINGLE LINE DIAGRAM

SISTEM DISTRIBUSI TENAGA LISTRIK - PABRIK MANUFAKTUR

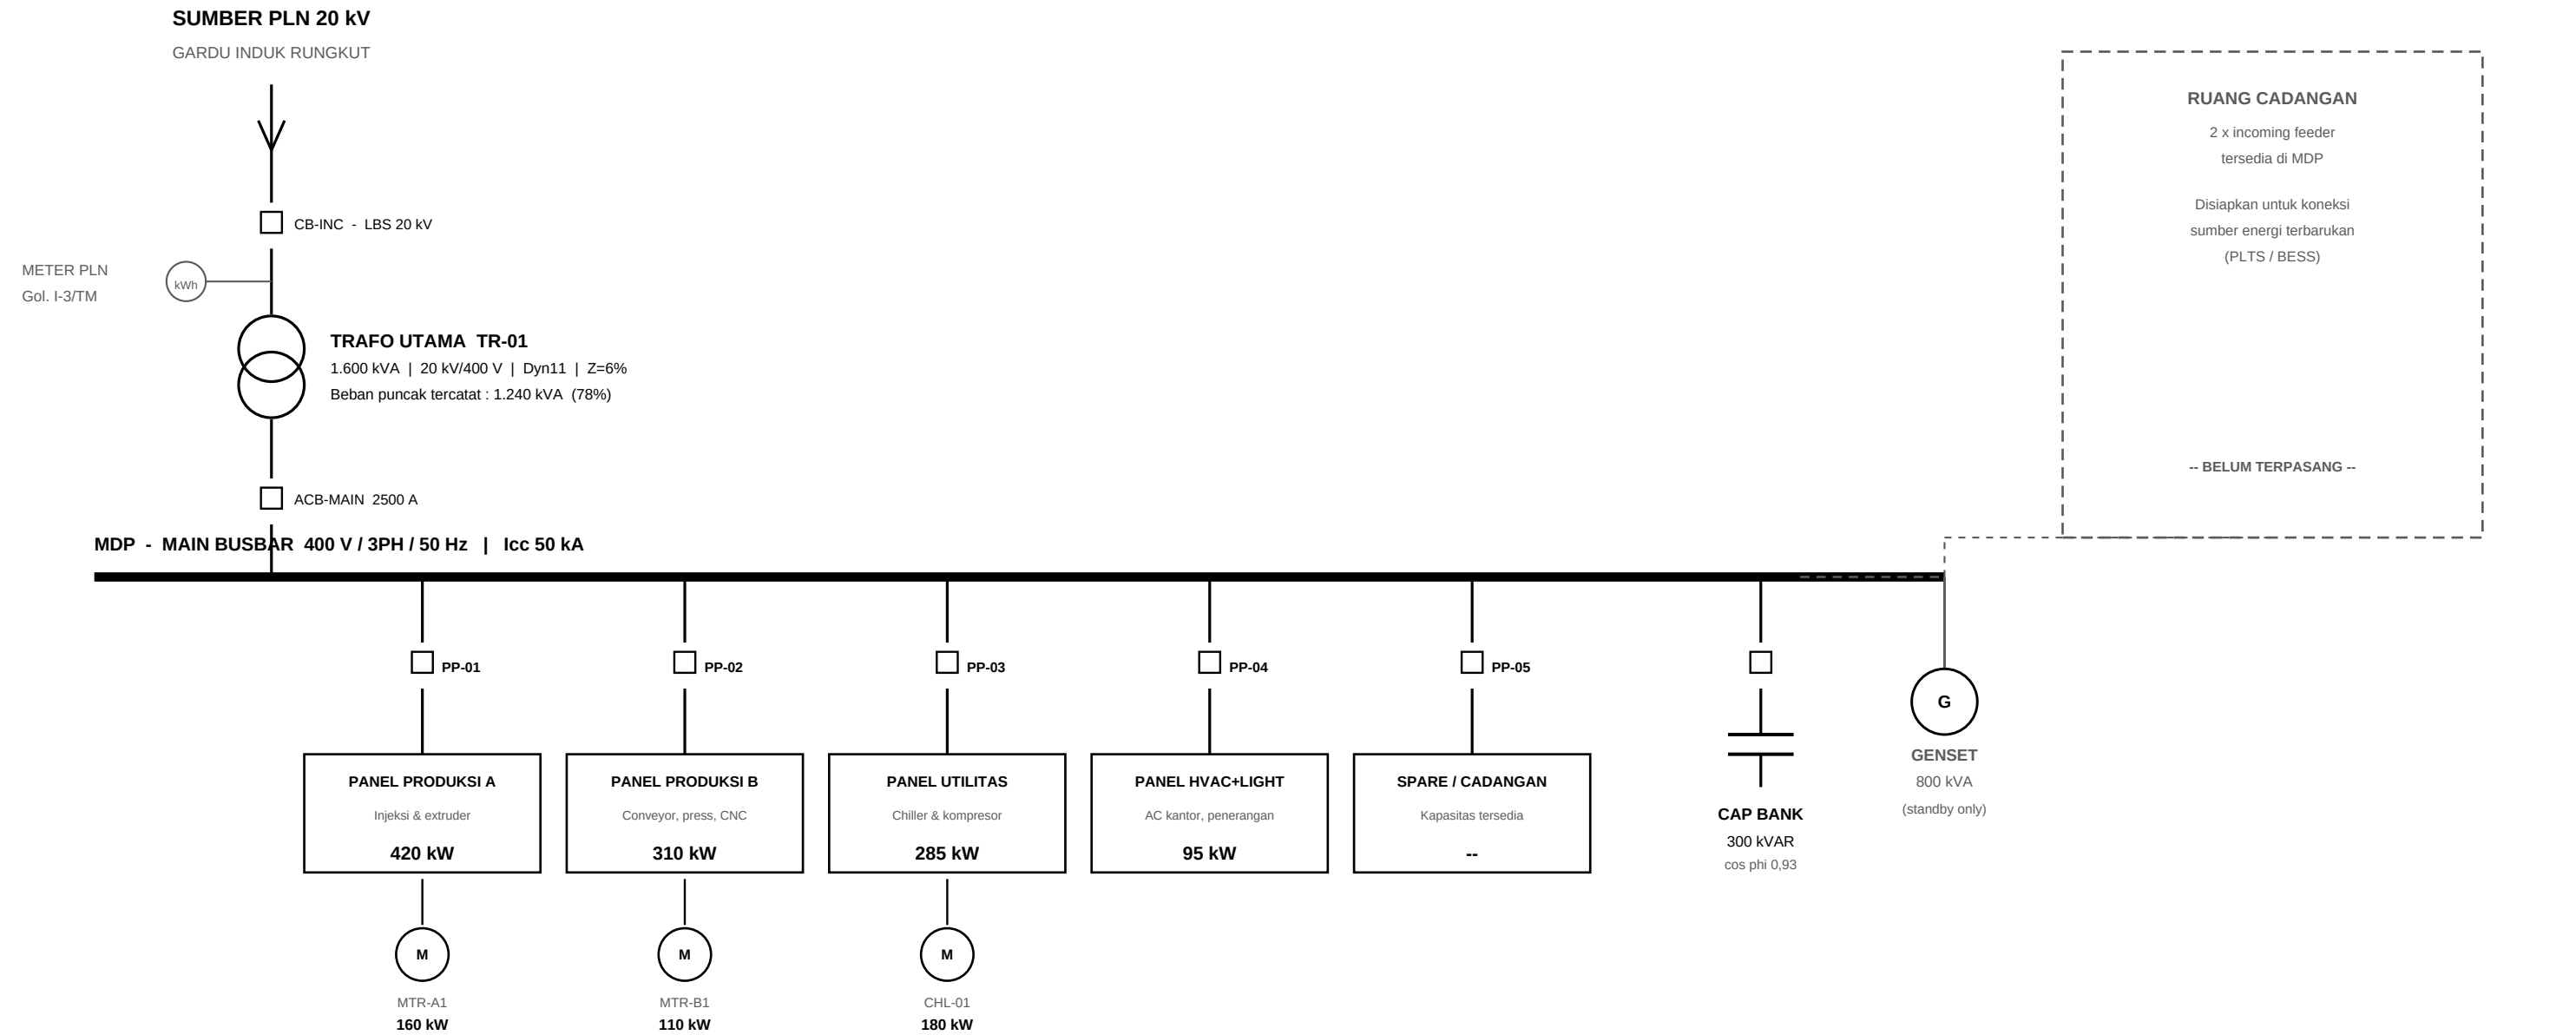

CATATAN INSTALASI & SITE	
1. Beban terpasang	: 1.110 kW
2. Beban puncak tercatat	: 1.240 kVA (~1.153 kW)
3. Beban dasar malam (sh-3)	: +/- 380 kW konstan
4. Luas atap (prod+gudang)	: +/- 8.400 m2
5. Orientasi atap	: Timur-Barat, 10 deg
6. Kapasitas trafo tersisa	: 360 kVA (headroom 22%)
7. Belum ada PLTS / BESS.	

PT SURYA MANUFAKTUR NUSANTARA	
Kaw. Industri SIER Blok D-14, Rungkut - Surabaya	
SINGLE LINE DIAGRAM - INSTALASI UTAMA	
DWG : SMN-ELE-SLD-001 TGL : 12 MEI 2026	REV : 03 NTS 20 kV / 400 V